00026-901-002

Восстановленный подлинник № 1

№ п/п	Наименование	Обозначение
	Вспомогательные документы	
1	Теоретический чертеж внутреннего корпуса	00026-901-003
2	Теоретический чертеж жесткого закрытия	00026-901-004

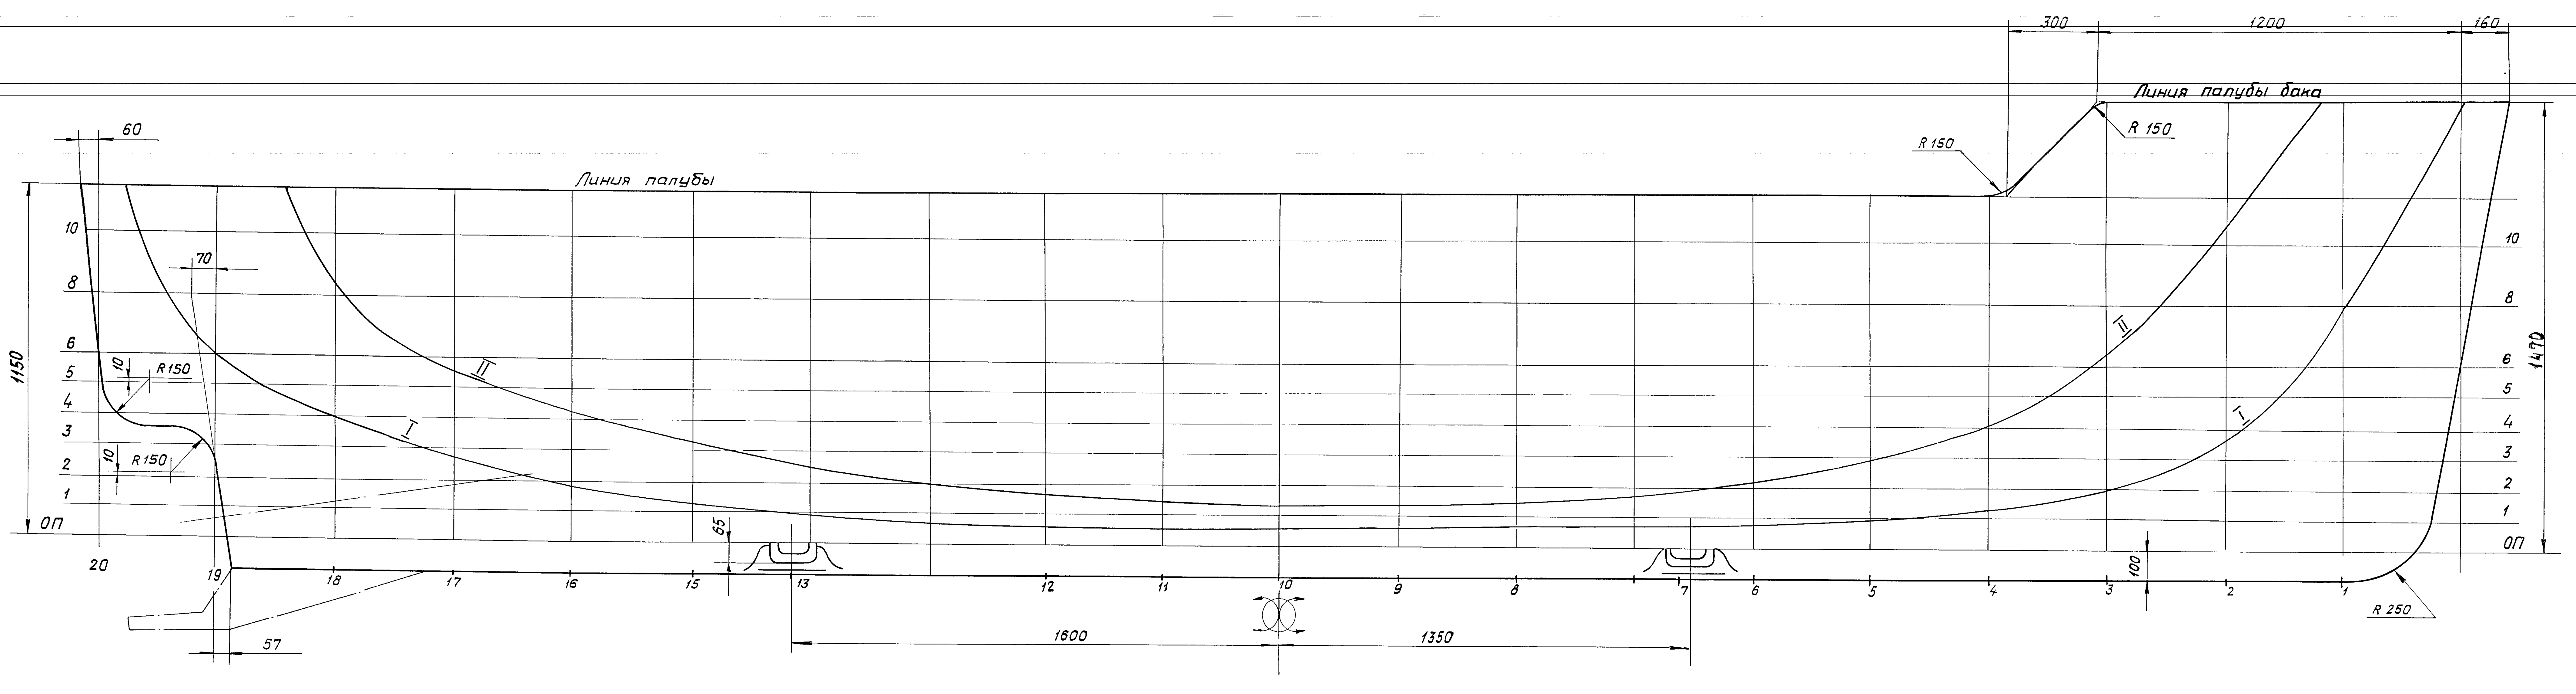

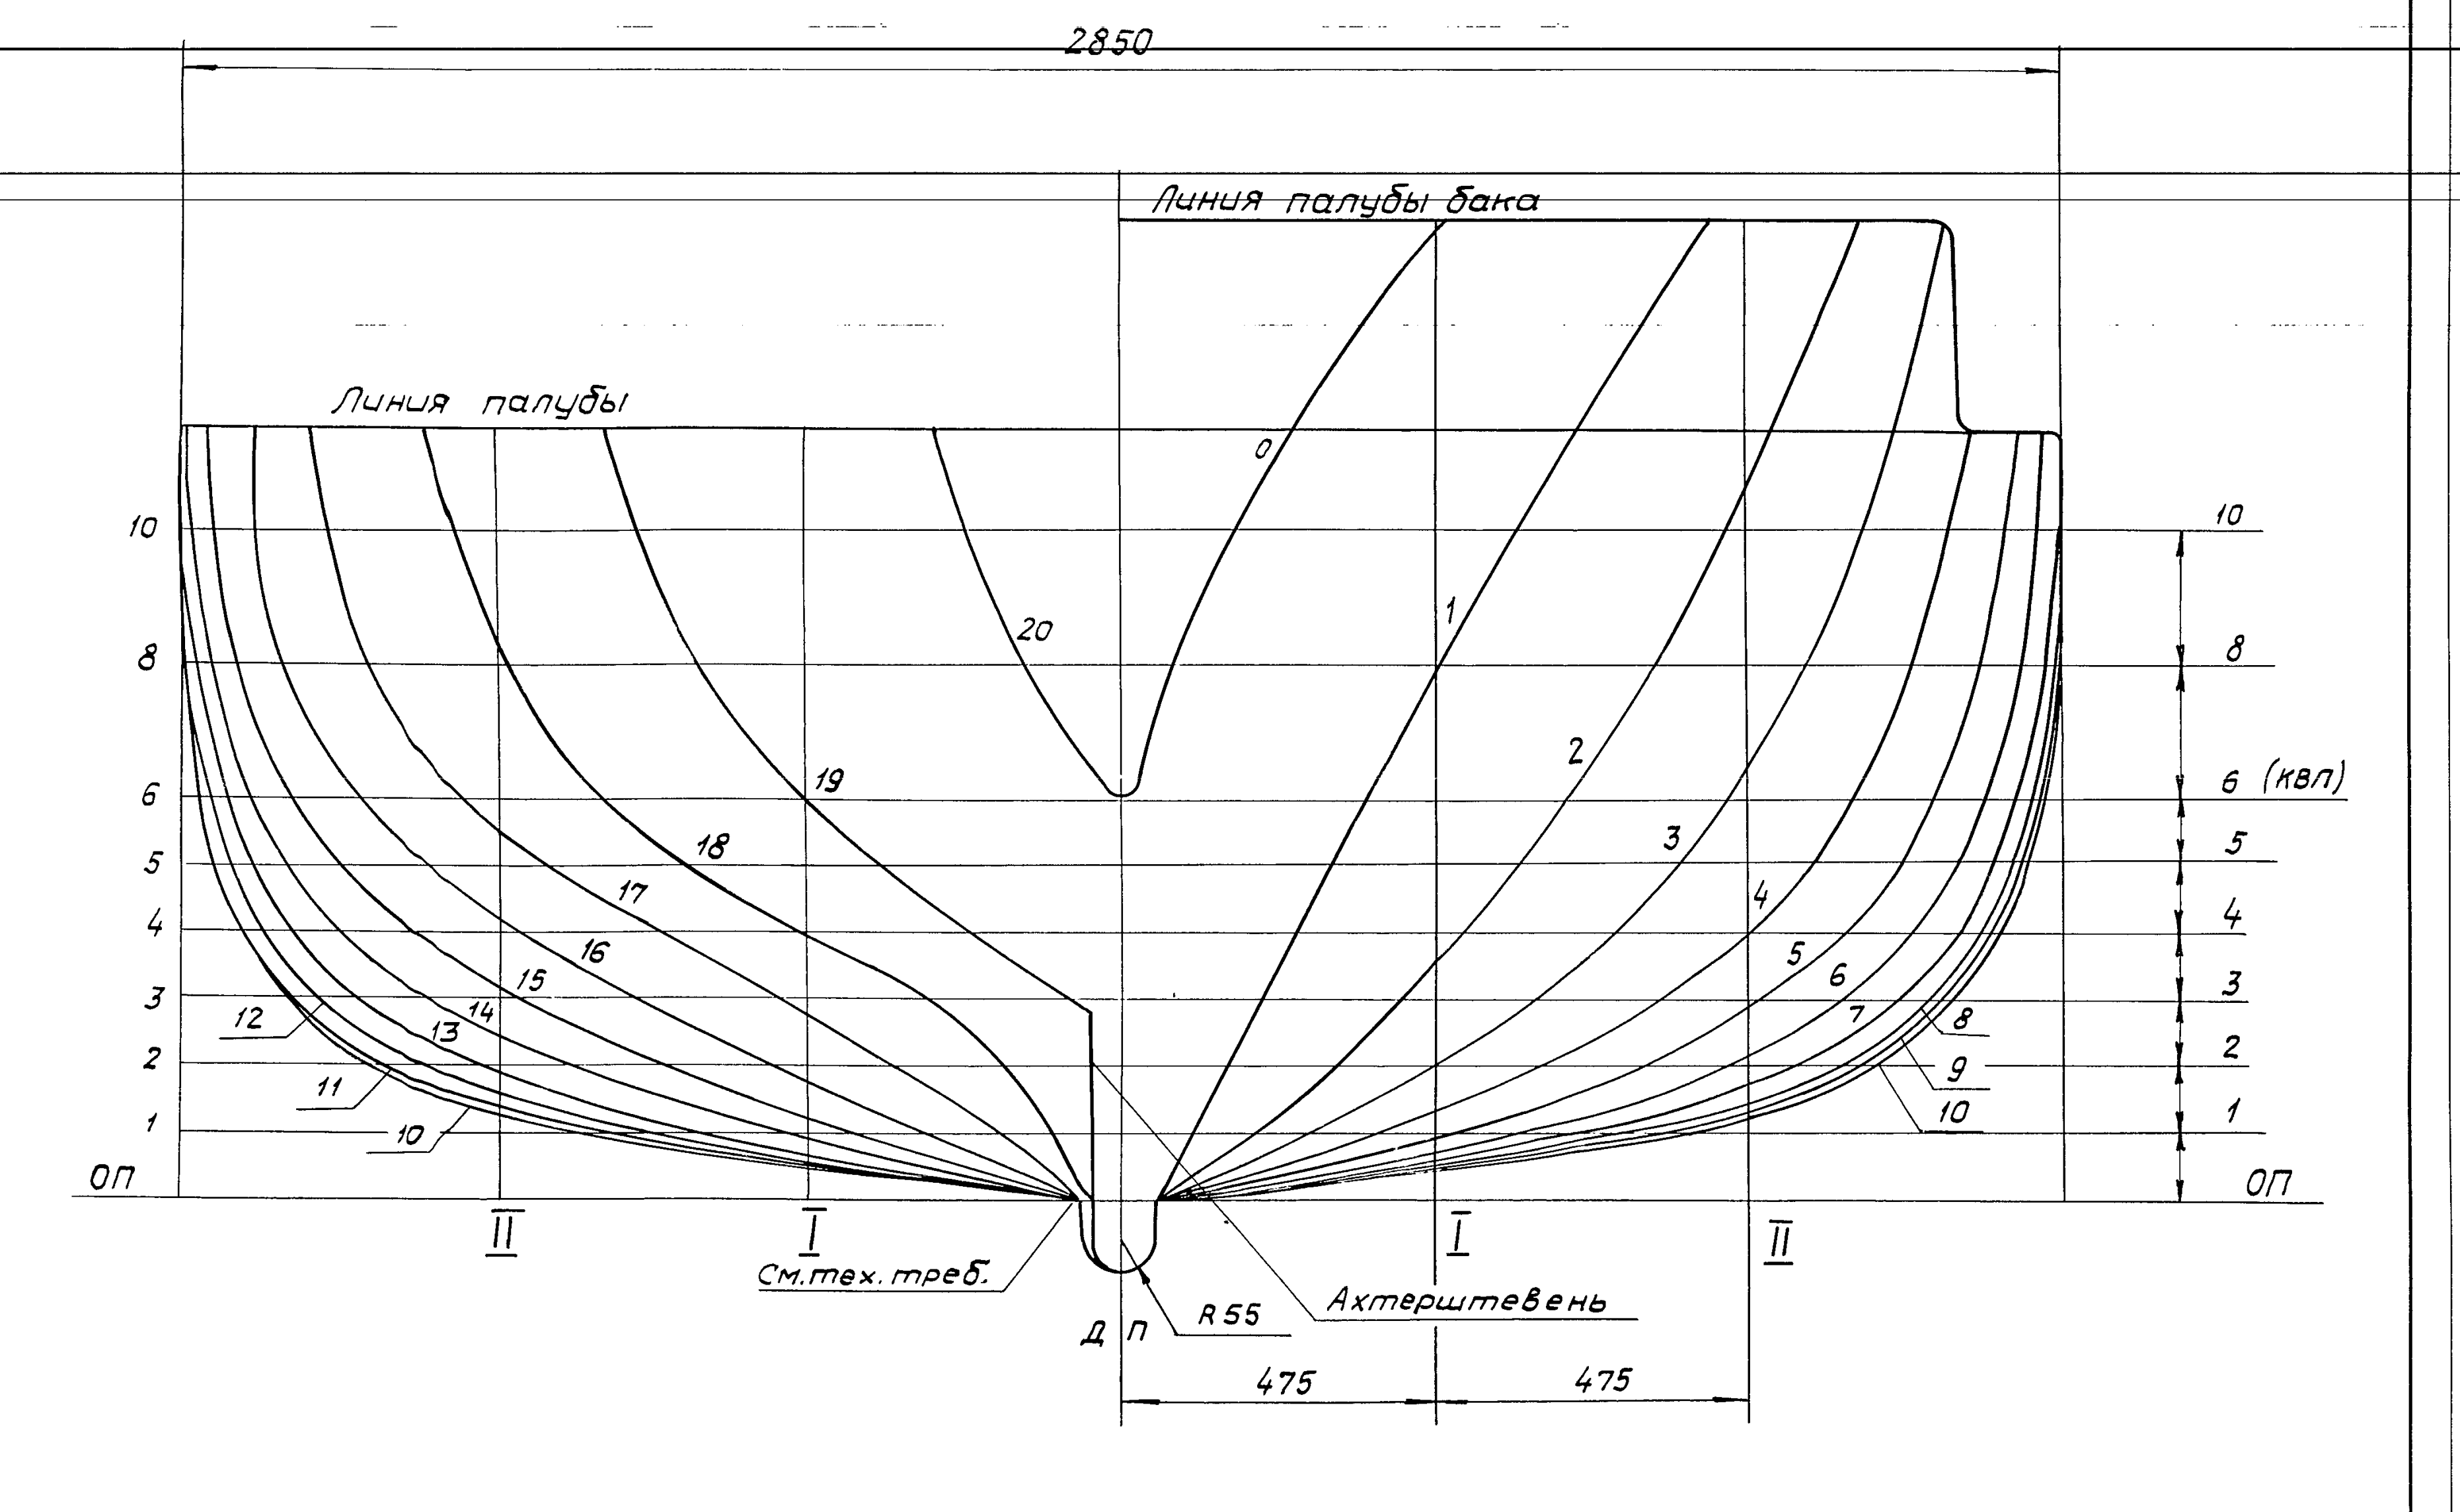

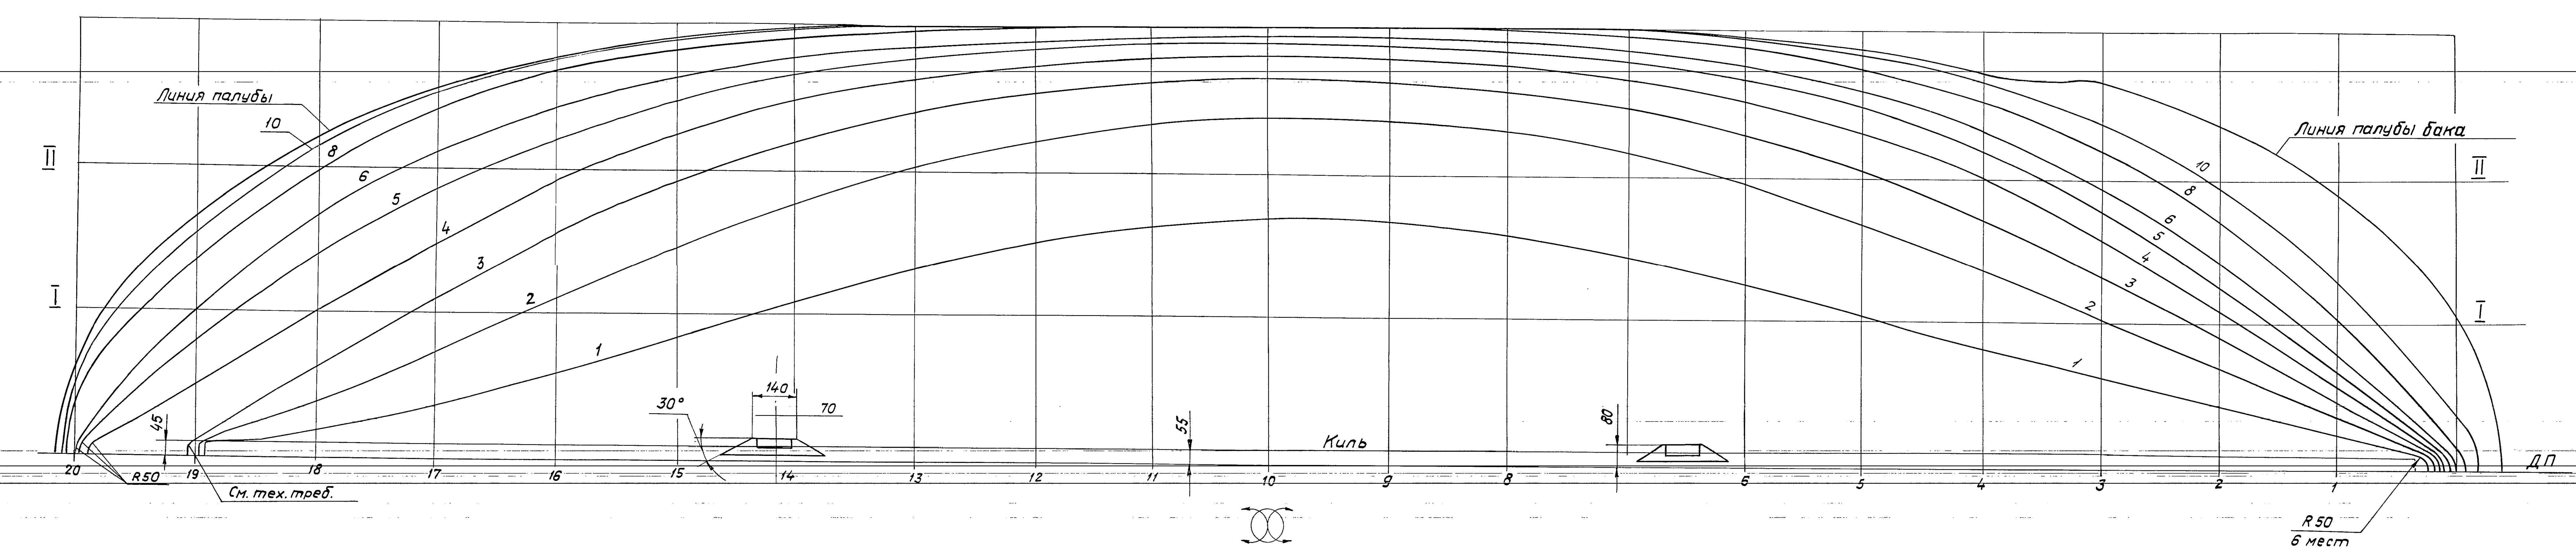

Таблица плазовых ординат.

№ шп.	Полушироты от ДП мм									Высоты от ОП мм		№ шп.
	Ватерлинии								Палуба	Батоксы		
	1	2	3	4	5	6	8	10		I	II	
0	—	—	—	—	—	0	80	175	490	1450	—	0
1	109	161	213	266	318	371	485	605	891	783	—	1
2	198	321	426	517	598	671	802	914	1110	353	1073	2
3	291	483	630	745	836	910	1030	1119	1250	195	661	3
4	388	640	814	938	1030	1096	1192	1251	1280	131	412	4
5	485	789	964	1083	1170	1230	1300	1339	1355	98	291	5
6	580	918	1081	1187	1260	1310	1364	1387	1397	80	216	6
7	670	1024	1169	1258	1316	1355	1396	1414	1420	69	170	7
8	748	1090	1222	1300	1349	1380	1413	1424	1425	60	144	8
9	795	1120	1245	1320	1364	1390	1417	1425	1425	55	132	9
10	811	1130	1256	1330	1372	1395	1420	1425	1425	53	129	10
11	792	1107	1240	1317	1365	1393	1420	1425	1425	54	138	11
12	728	1044	1200	1289	1345	1379	1415	1425	1425	57	162	12
13	625	957	1138	1245	1305	1358	1410	1416	1420	70	197	13
14	519	837	1043	1173	1259	1317	1379	1400	1405	89	249	14
15	399	687	907	1063	1175	1253	1340	1370	1374	125	324	15
16	282	507	728	909	1050	1151	1269	1302	1308	185	425	16
17	174	321	515	708	878	1000	1135	1188	1205	280	553	17
18	92	162	289	474	656	787	930	1006	1040	400	838	18
19	—	—	58	233	372	484	641	733	780	591	—	19
20	—	—	—	—	—	0	145	234	275	—	—	20

Главные размерения.

Длина наибольшая	$L_{нб}$ = 8,0 м
Длина между перпендикулярами	$L_{⊥⊥}$ = 7,78 м
Ширина наибольшая	$B_{нб}$ = 2,85 м
Высота борта на миделе	H = 1,15 м
Расстояние между теоретическими шпангоутами	ΔL = 0,389 м

Таблица плазовых ординат откорректирована по данным разбивки на плазе.

Технические требования.
Радиусы скруглений выполнить по конструктивному чертежу.

Годен
для пр. 00326

ГОДЕН
для пр. 00265

ⓓ

Балтийская инспекция Регистра СССР
Старший инженер-инспектор   Подпись / Маркелов /
06.03.86.

Изм.	Лист	№ докум.	Подпись	Дата
д		00026.11.308		27.05.93
г		00026.11.185.	Подп. -	26.05.87.
Разраб.		Сиванов	Подп.	5.05.82.
Провер.		Сапожник	Подп.	11.08.82.
Вып.		Никифоров	Подп.	12.08.82
Т. контр.		Кузнецов	Подп.	
Н. контр.		Рязанцева	Подп.	16.08.82.
Утв.		Абрамов	Подп.	12.08.82.

00026-901-002

Теоретический
чертеж наружного
корпуса.

Лит.	Масса	Масшт.
		1:10
Лист	Листов 1	

Предприятие
п/я В-8458

Формат 26   пл. 0,75 м²

Инв.№ подл.	Подпись и дата	Взам.инв.№	Инв.№ дубл.	Подпись и дата
51480	Подп. 17.08.82.			

Справ. №	Перв. прим.

Восстановлен с подлинника.
Верно: 7.12.91. Мяэзыта А.А.
Подпись Фамилия Дата