




Система Водяного охлаждения
черт. 02020.362463.002

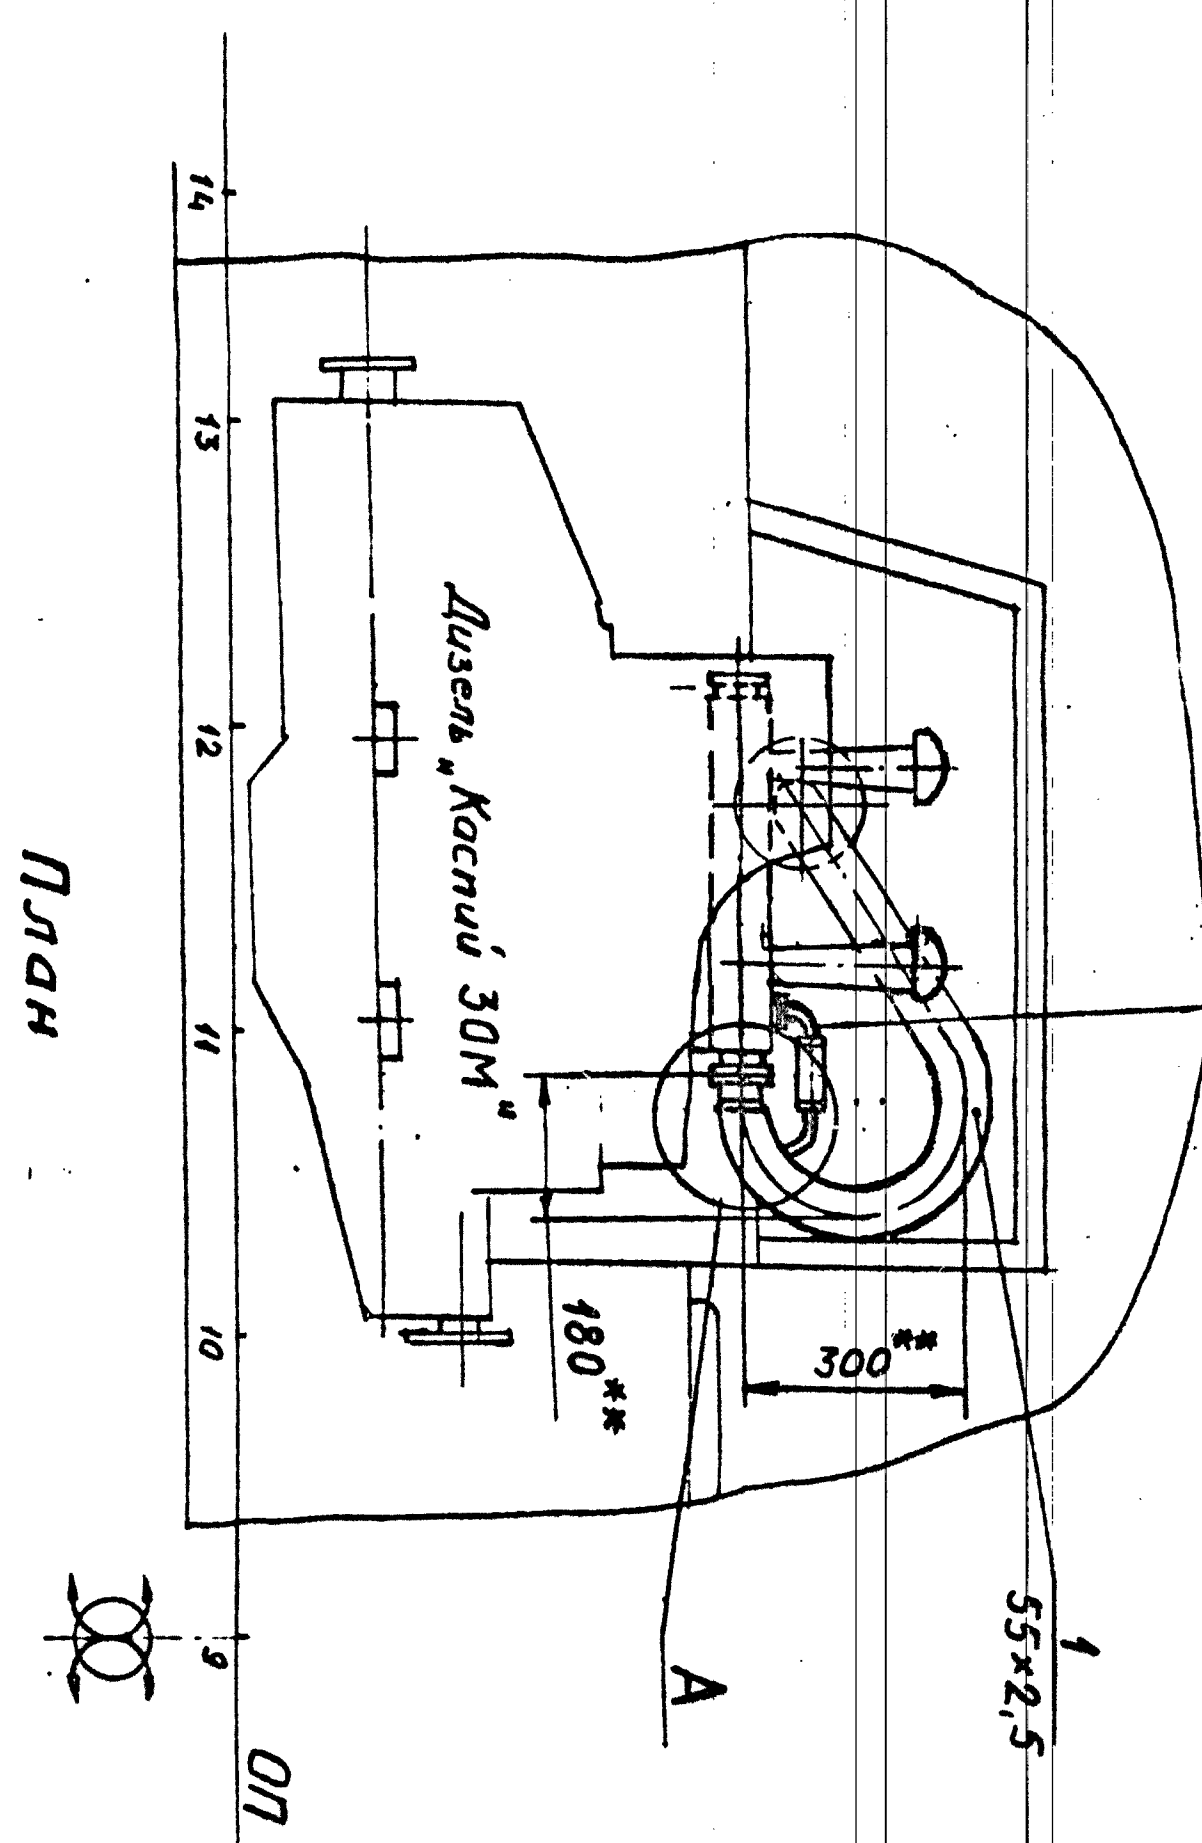




П

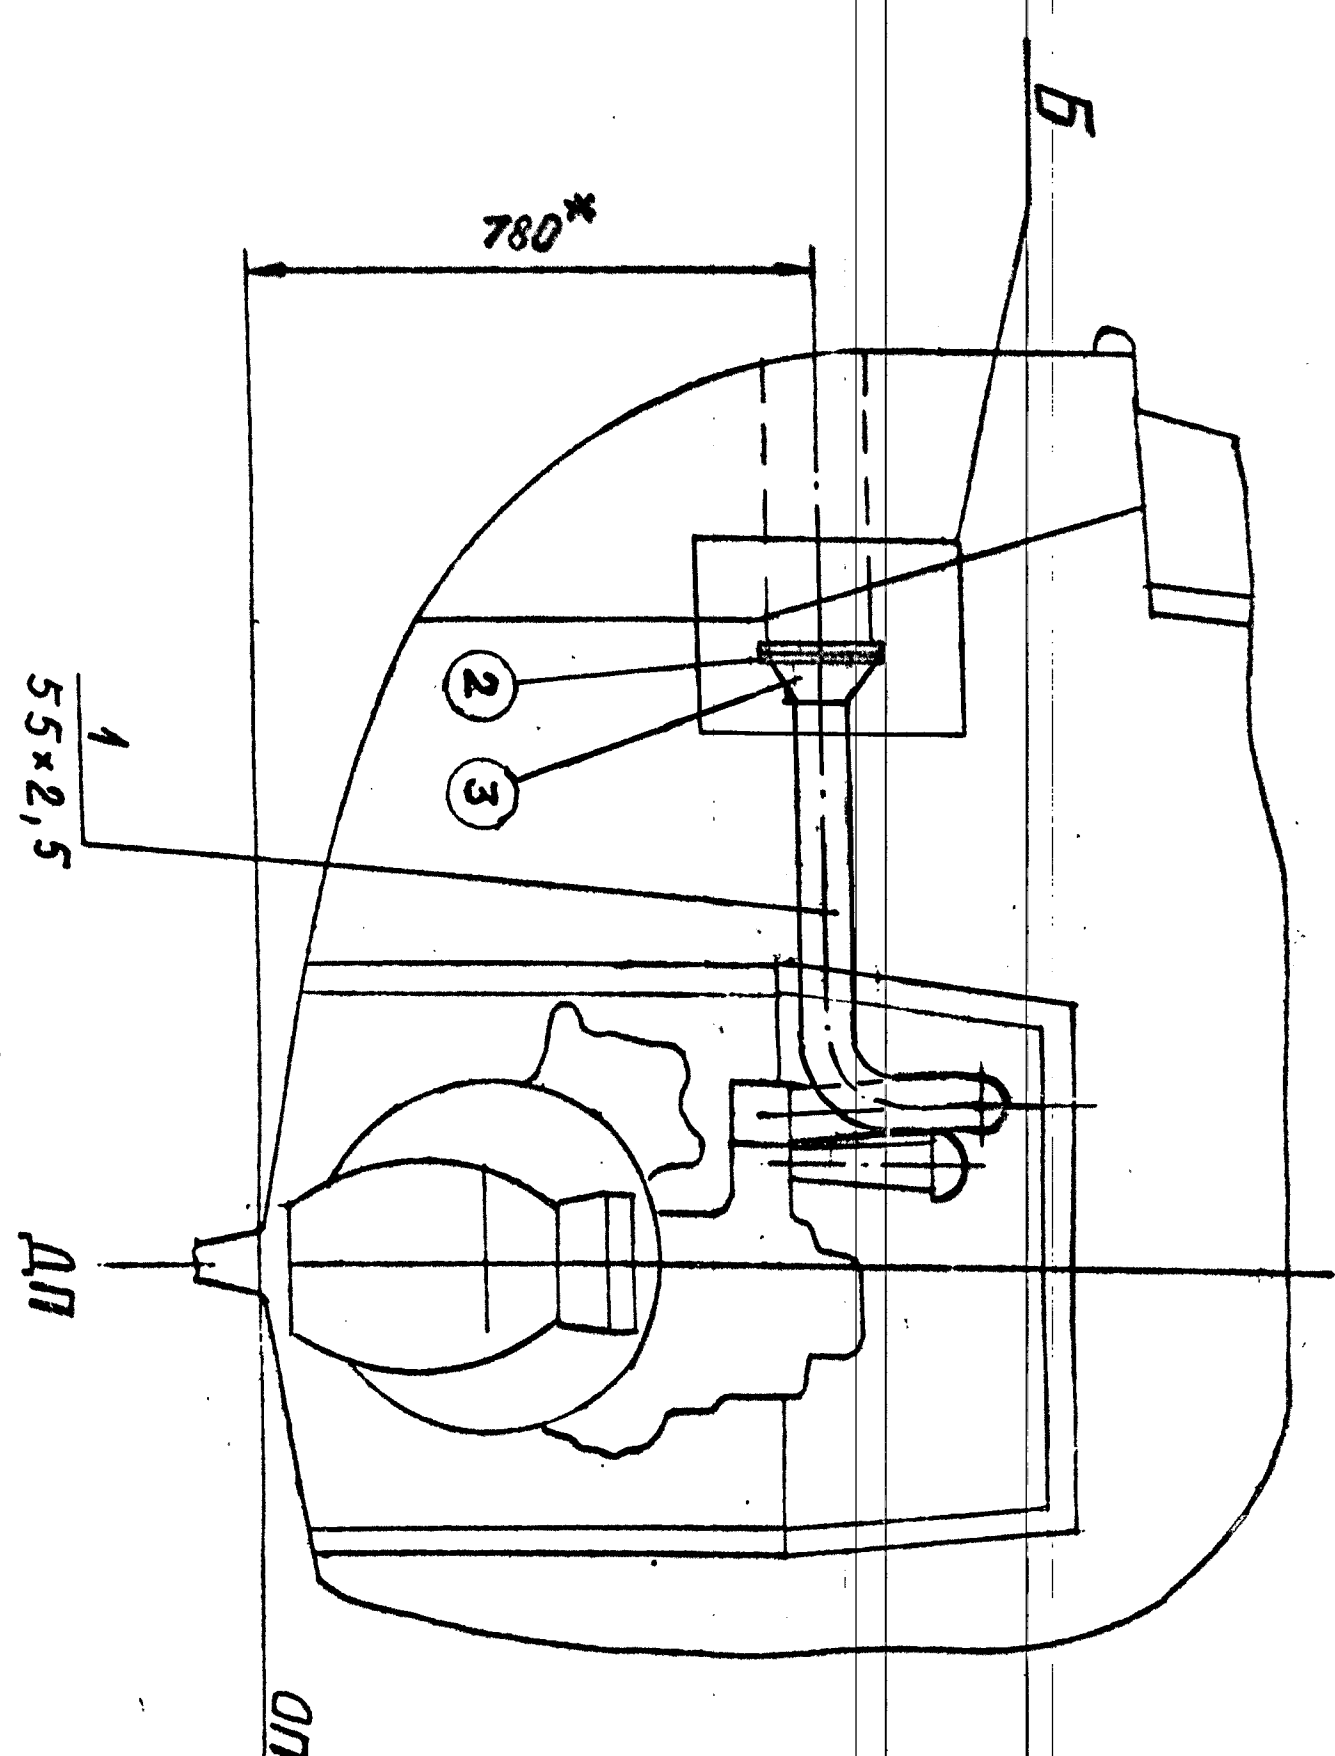

5 (1:1)

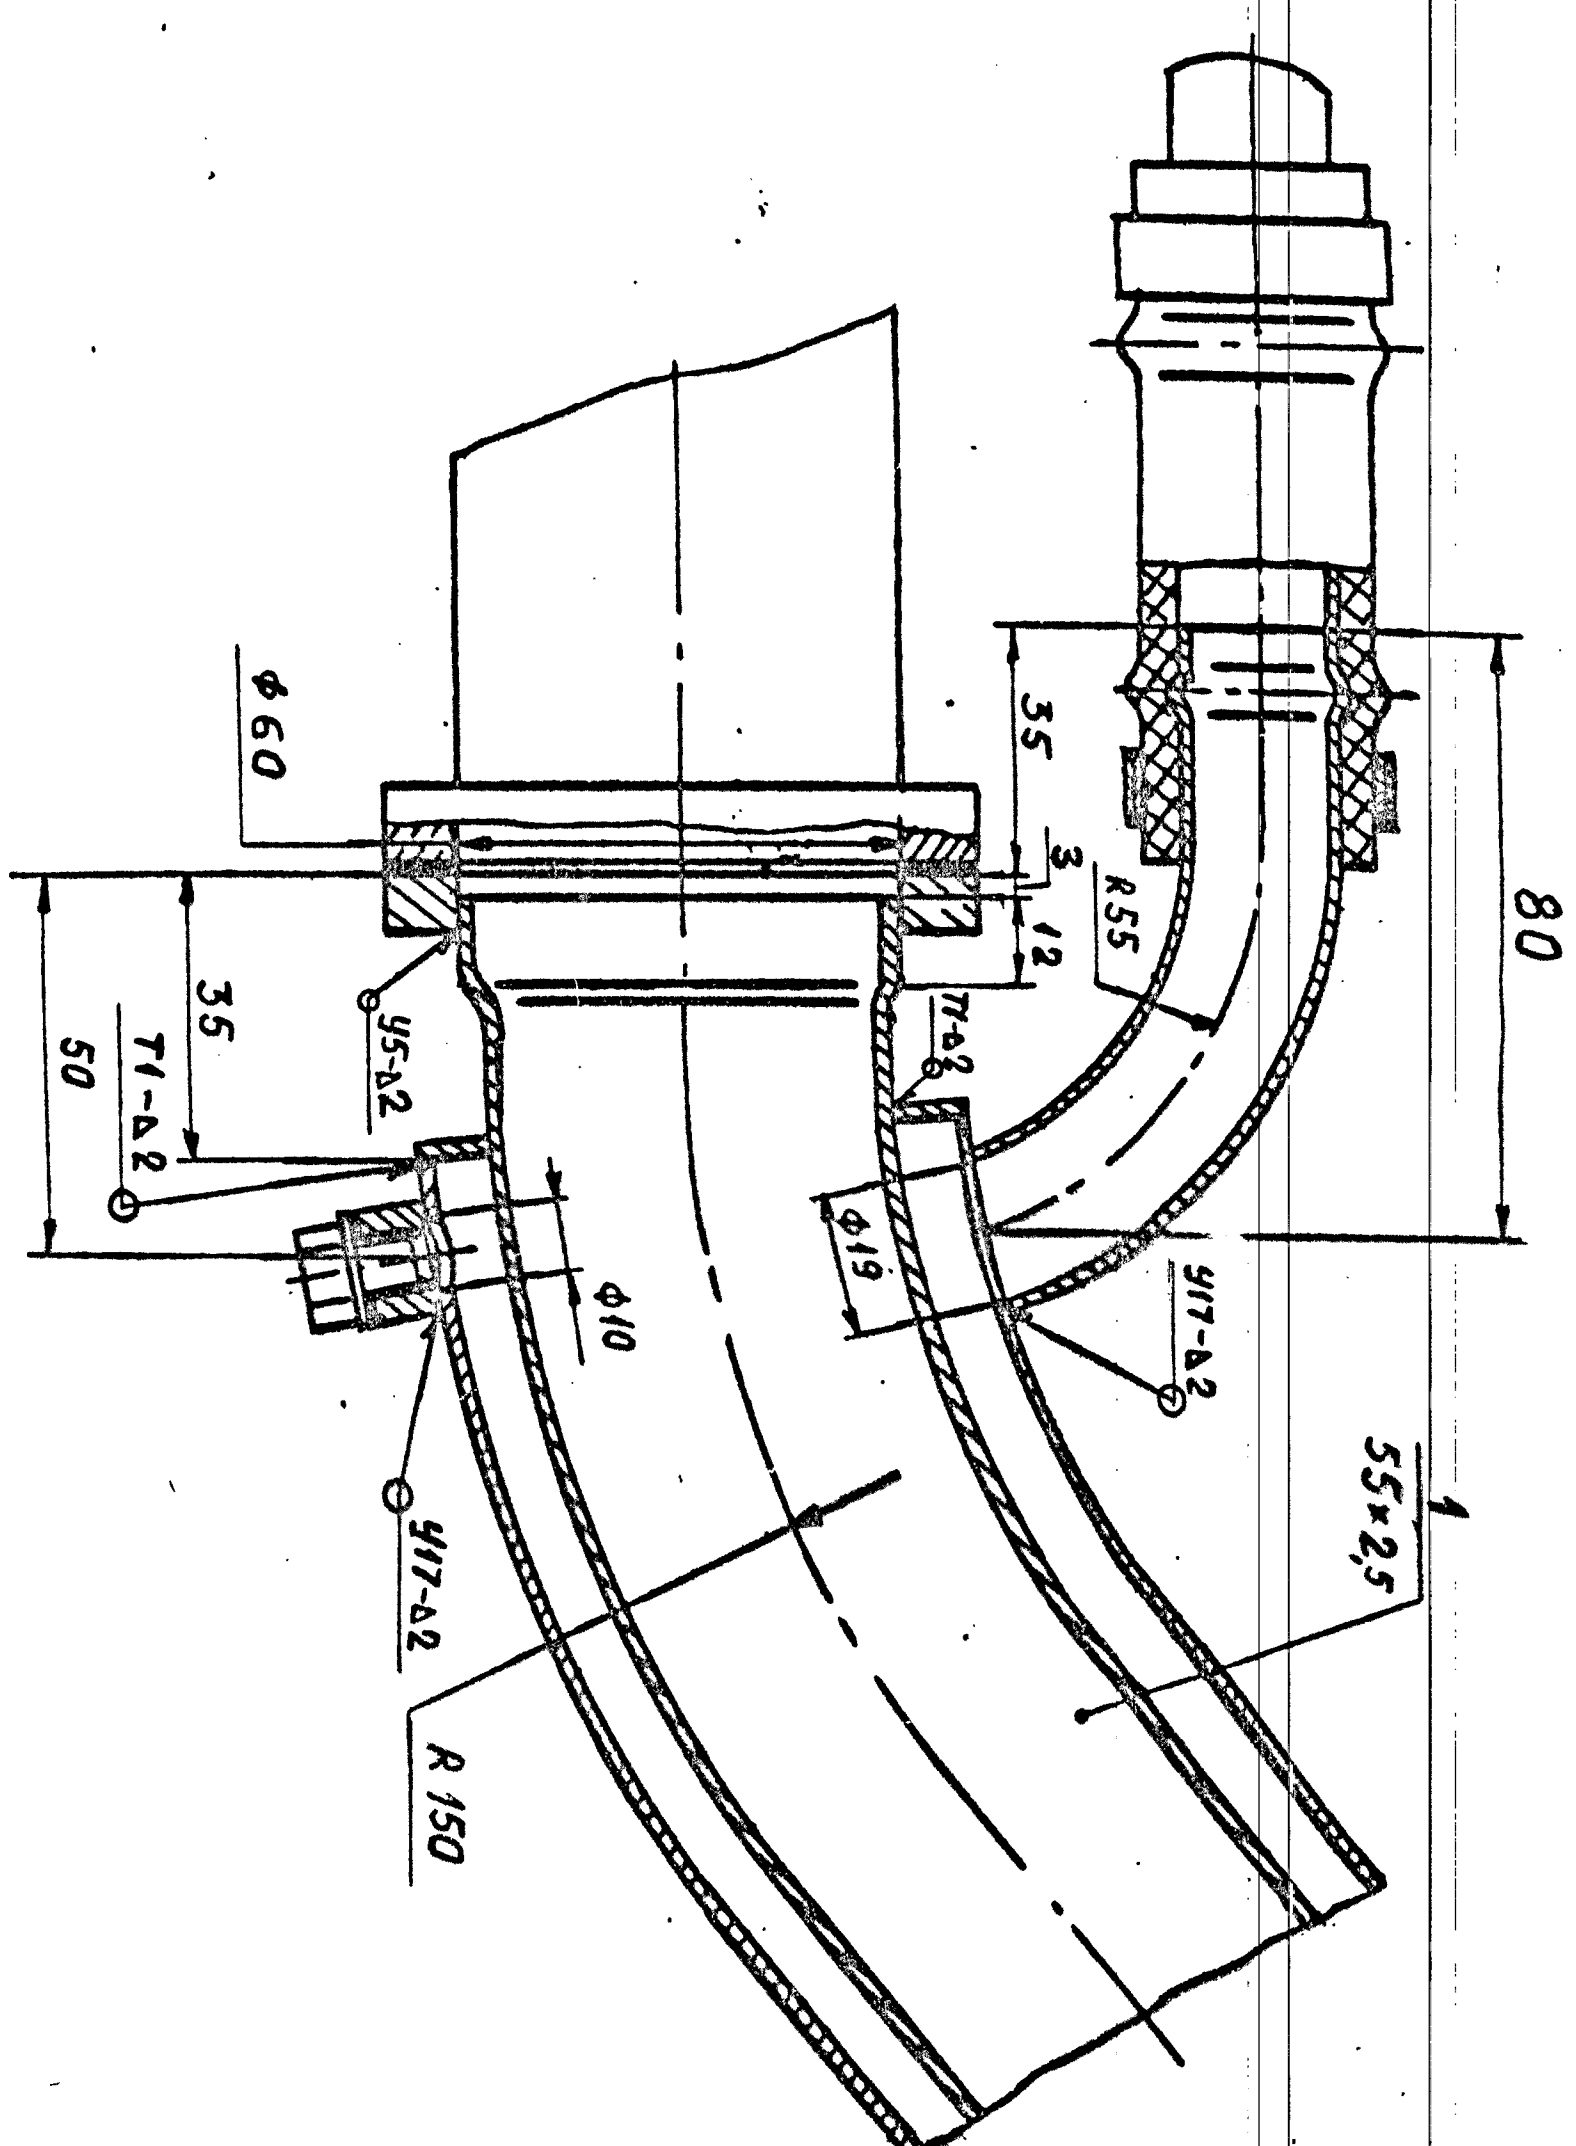

Тубовой узел усмановки
железек

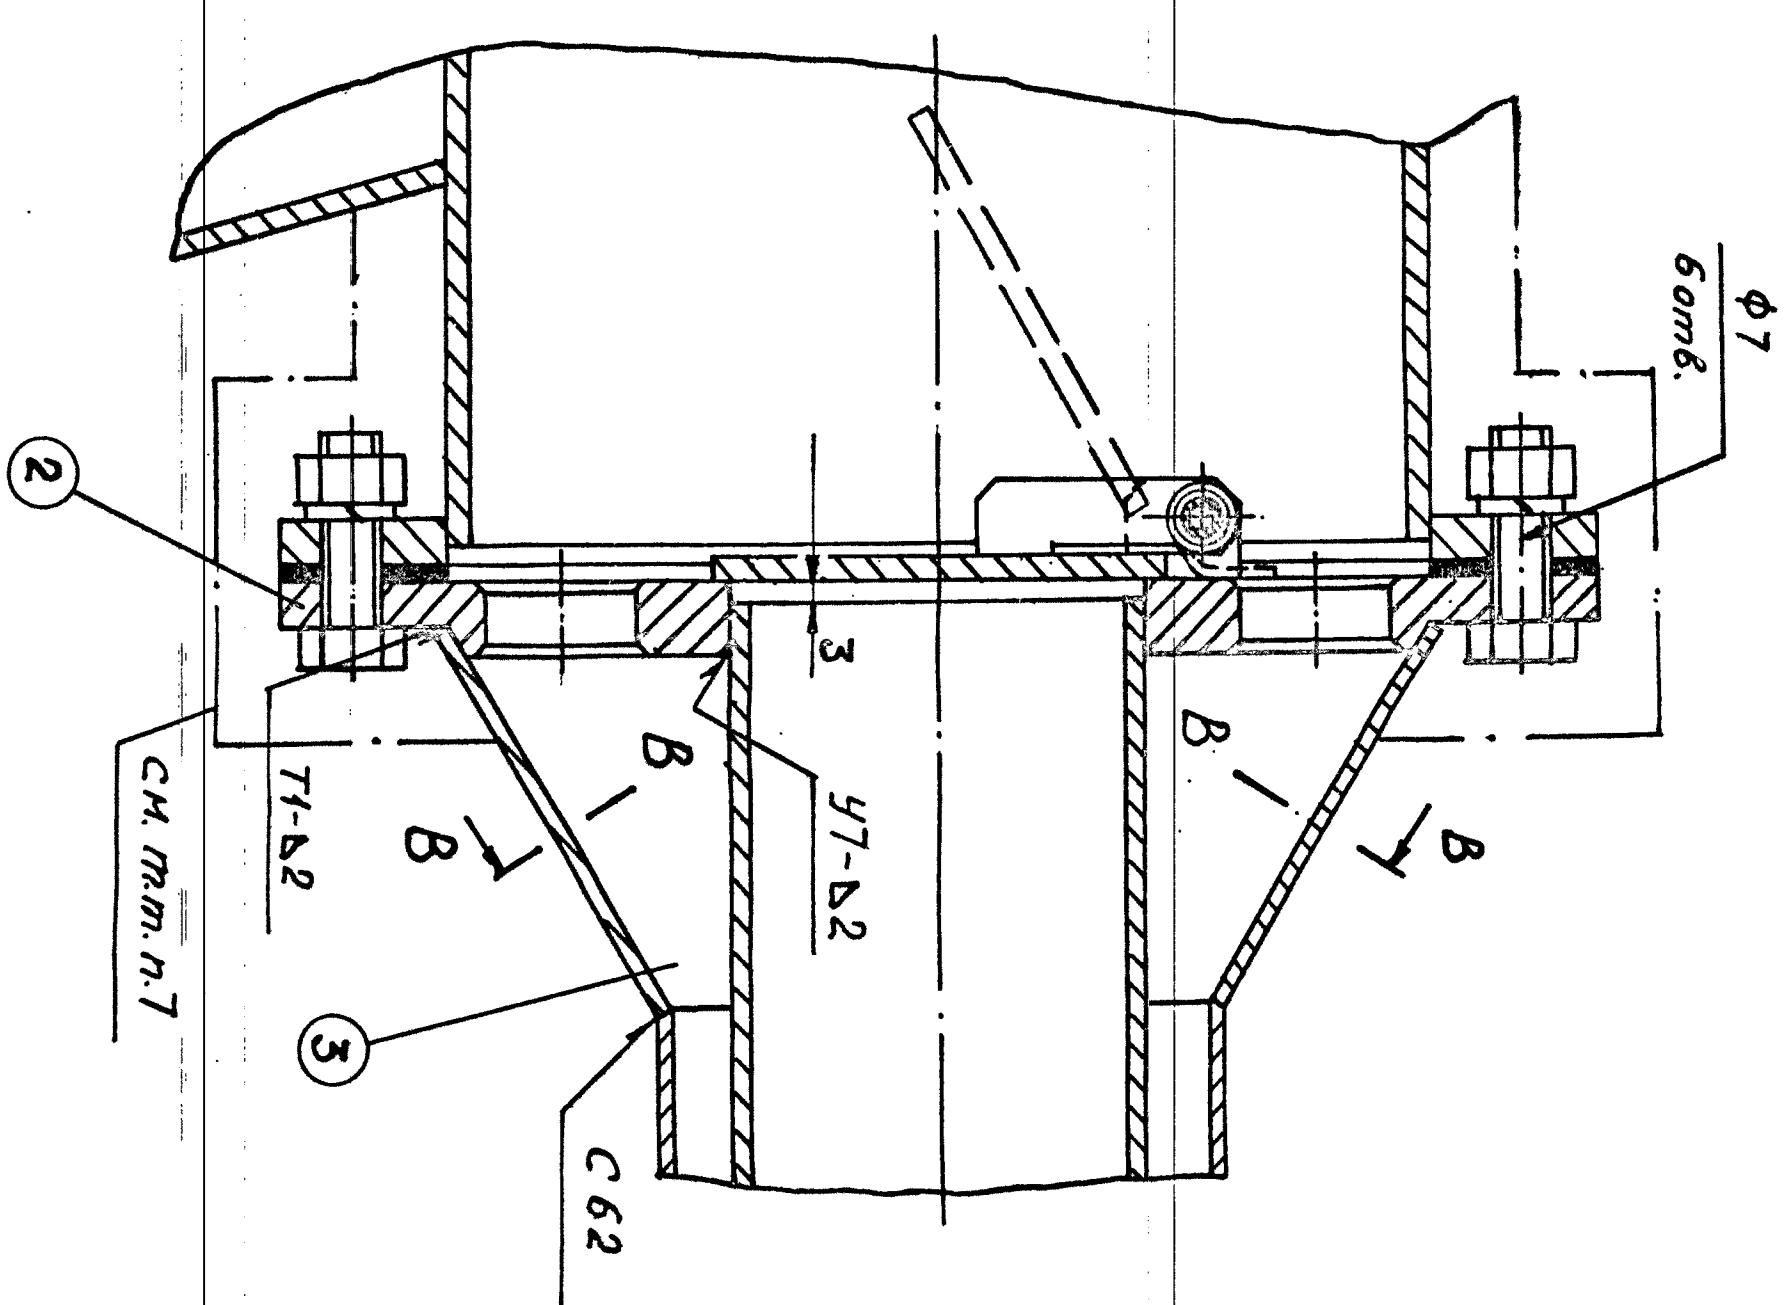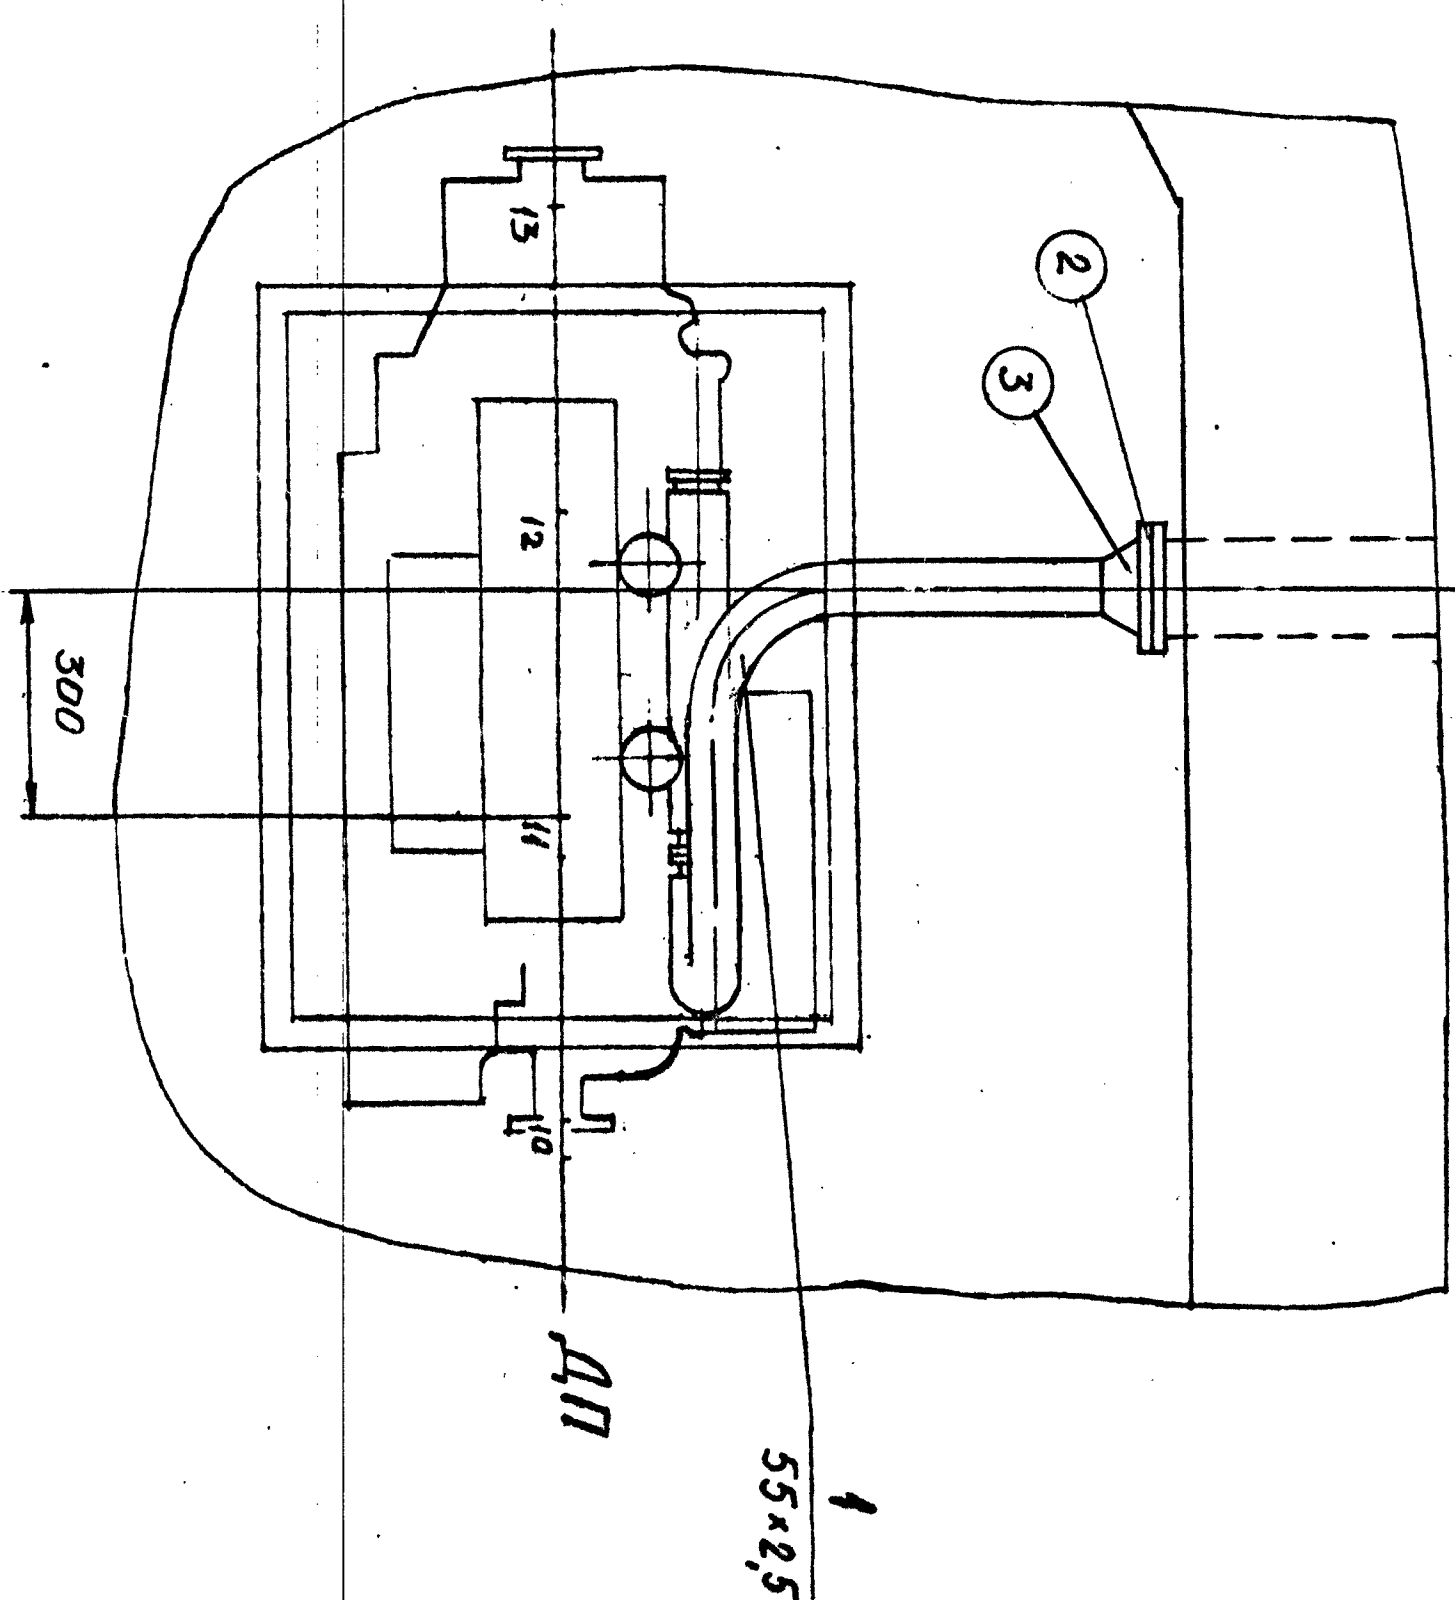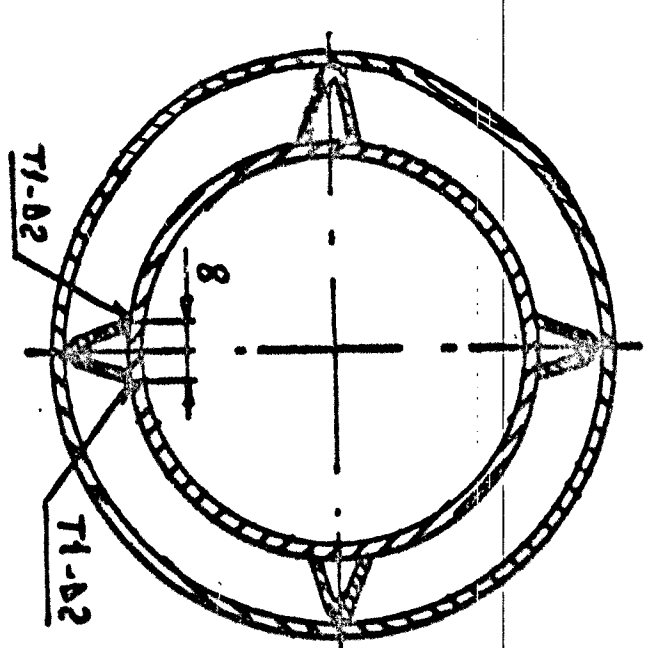

B-B (1:1) $\odot$
C4

Вспомогательные документы	Обозначение
Наименование	
Общие расположенные нехому- ветровой установка	020200.302421.001

1. При изготовлении и монтаже системы руководитель базируется ИАТ.360x508.005(210-185.553).
2. Труды перед монтажом усилить по другим III ДСТ 5.9523-81.
3. Сварка по ДА.5.9111-83. Конструктивные элементы шва по ДСТ 5.9088-81.
4. Жердильки расположить в шахматном порядке с шагом: в местах повода трубовода - 700 мм на прямых участках трубы - 200 мм.
5. Газовую полость трубы поз. 1 усилить на прочность сварочным давлением $P=0,2 \text{ МПа}$ и на плотность воздушным давлением $P=0,2 \text{ МПа}$ водную полость испытать на плотность воздушным давлением $P=0,2 \text{ МПа}$. Систему в сборе испытать на шланге в течение 5 минут.
6. Прокладку и крепеж фланца закладки поз. 2 установить на термике У30 МЭС-Б ДА.5.9656-85.
7. Выходную трубу 2 заложить поз. 2 изолировать слоем теплоизоляции толщиной 100 мм и обшить парусиной.
8. Покрытые крепежа по ДСТ 5.9048-85.
9. Проектильные отклонения размеров: мм , мм , $\pm \frac{1}{2}$.
10. * Размеры для справок.
11. * Размеры уточнить по месту.

ГОДЕН для проек-
та с дзевенем
"Качнуу-40"

Знамя	Басека	22.05.03
Подр.	Фамилия	Подп. Аном

Создано

[illegible]

Формат А2х5 Ил. 0,75м²