



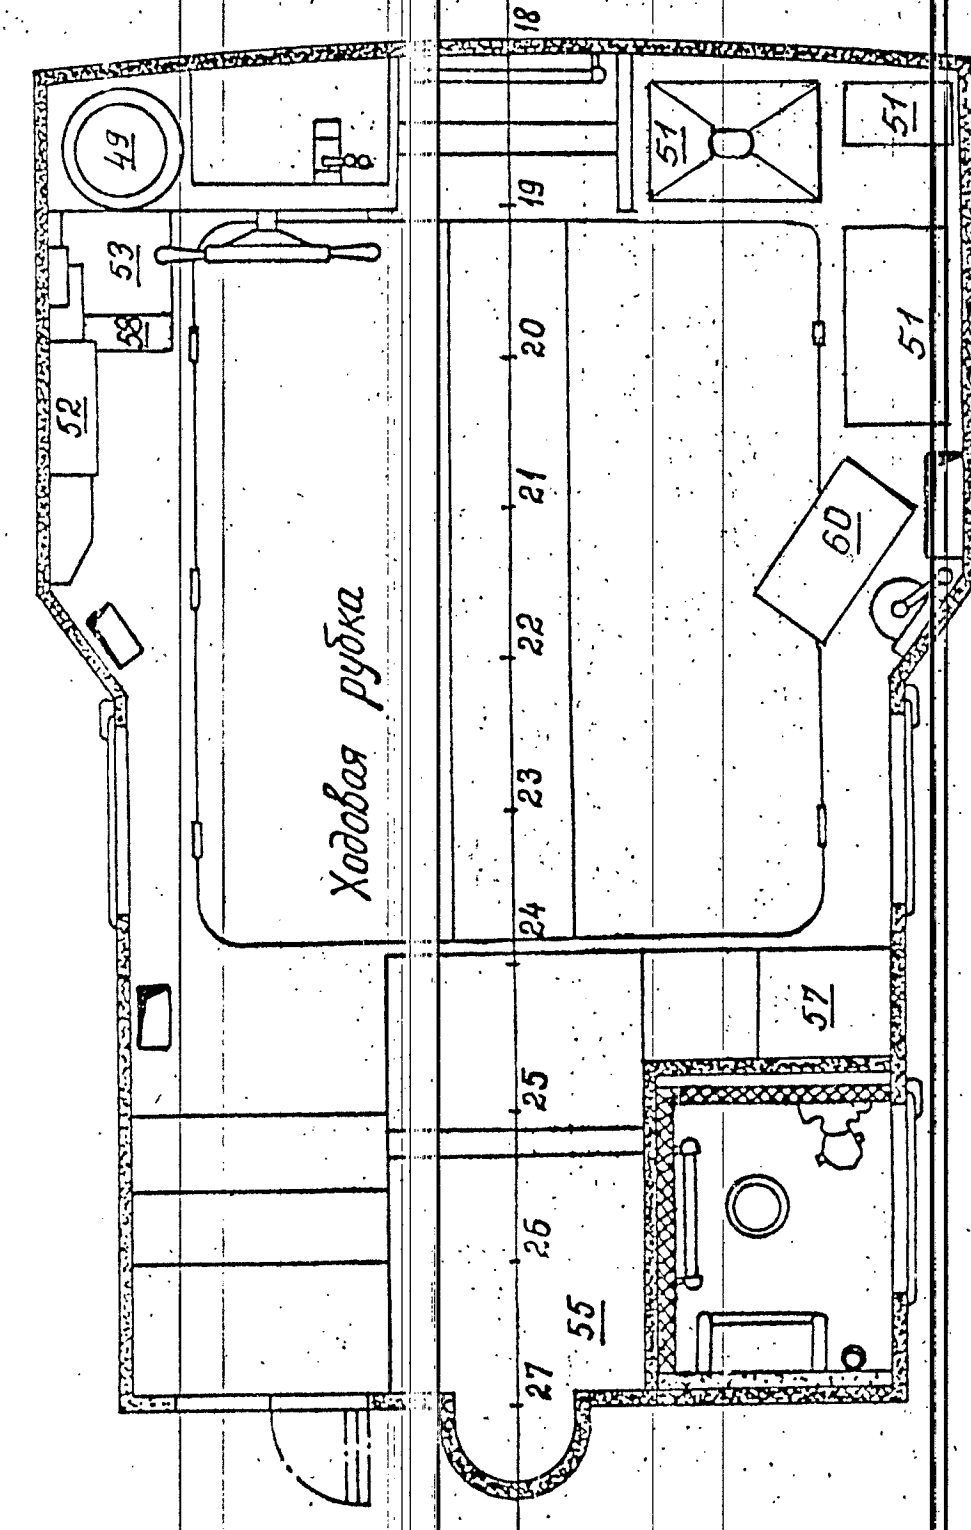

План со снятой палубой

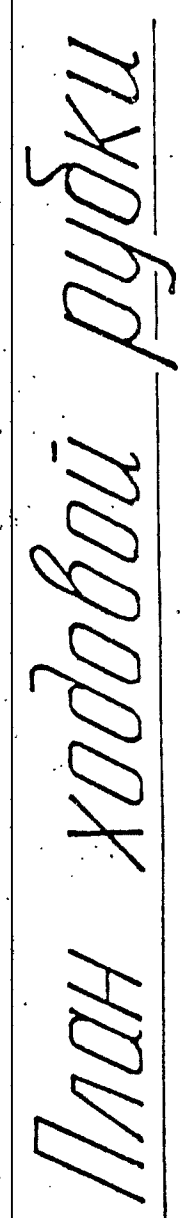