


М.Х

940-106-5141

Восстановленный подлинник №1

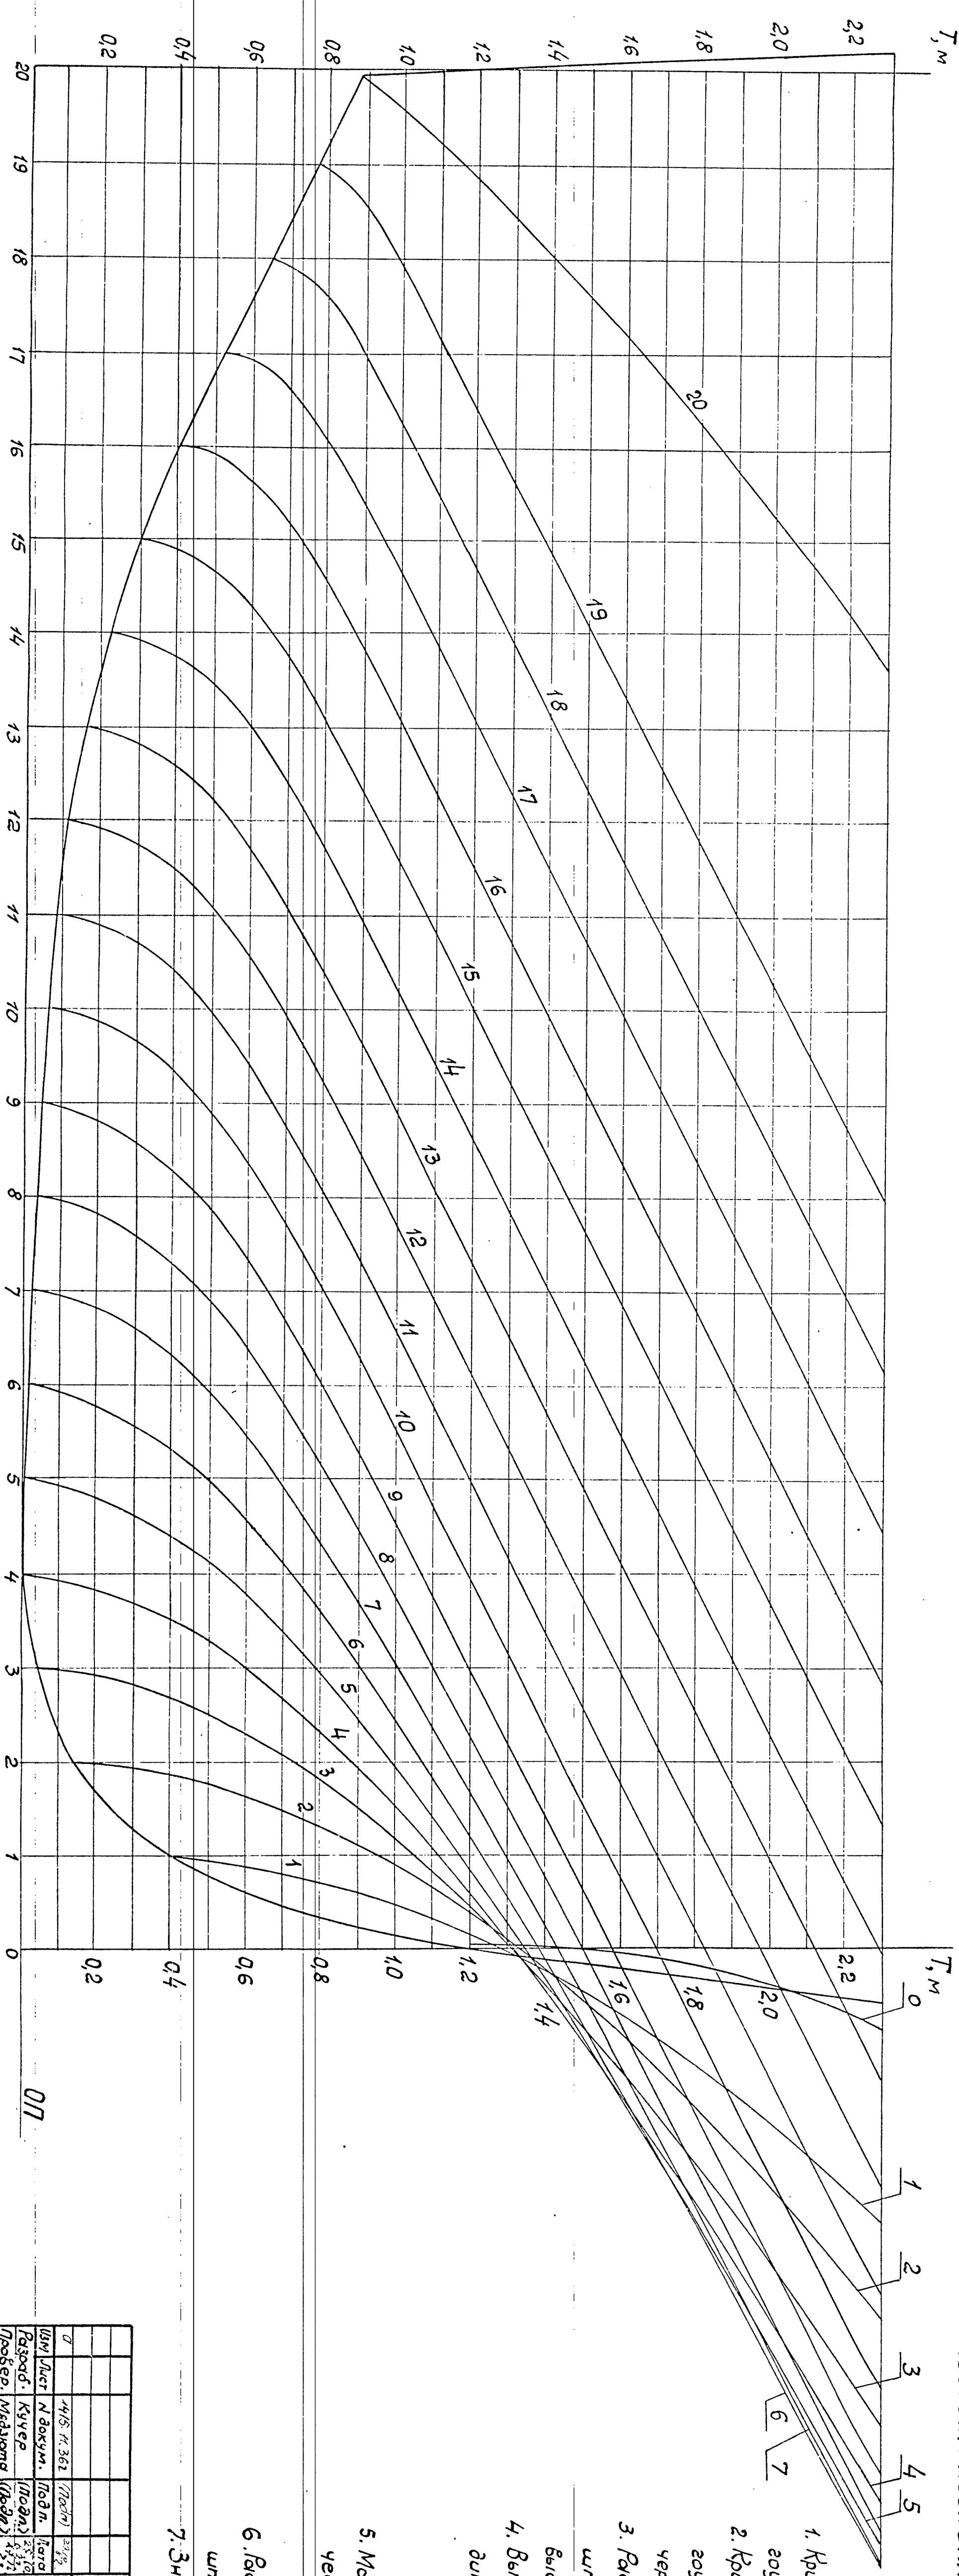

1. Кривые площадей теоретических шпандоутов построены по расчету 1415-901-046
2. Кривые площадей теоретических шпандоутов соответствуют теоретическому чертежу 1415-901-004.
3. Расчет площадей теоретических шпандоутов выполнен без учета выступяющих частей.
4. Вычисления водоизмещения произведены по формуле:

$$V = \Delta L \sum_{i=1}^{20} W_i$$

5. Масштаб кривых площадей теоретических шпандоутов 1 см - 0,2 м³
6. Расстояние между теоретическими шпандоутами $\Delta L = 1,0$ м
7. Значение площадей шпандоутов приведены.

Инв. № инв.	Подпись дата	Взам. инв. №	Инв. № докл.	Подпись дата
52237	01.11.82 (М.Х)	46264		

Восстановлен с подлинника
Верно: 28.03.85. (Васильев)
подл. дата фамилия

Шпандоутов	1415-901-046	Шпандоутов	1415-901-046
Размер: Кучер	1415-901-046	Размер: Кучер	1415-901-046
Выпуск: Семенов	1415-901-046	Выпуск: Семенов	1415-901-046
Н.контр. Ефимов	1415-901-046	Н.контр. Ефимов	1415-901-046
Удобр. Курбенов	1415-901-046	Удобр. Курбенов	1415-901-046

МФ Шейкина 29.04.85
МФ Шейкина 29.04.85

Формат 14

л. 0,25 м²