
00373-210-084 СБ


Восстановленный подлинник № 1

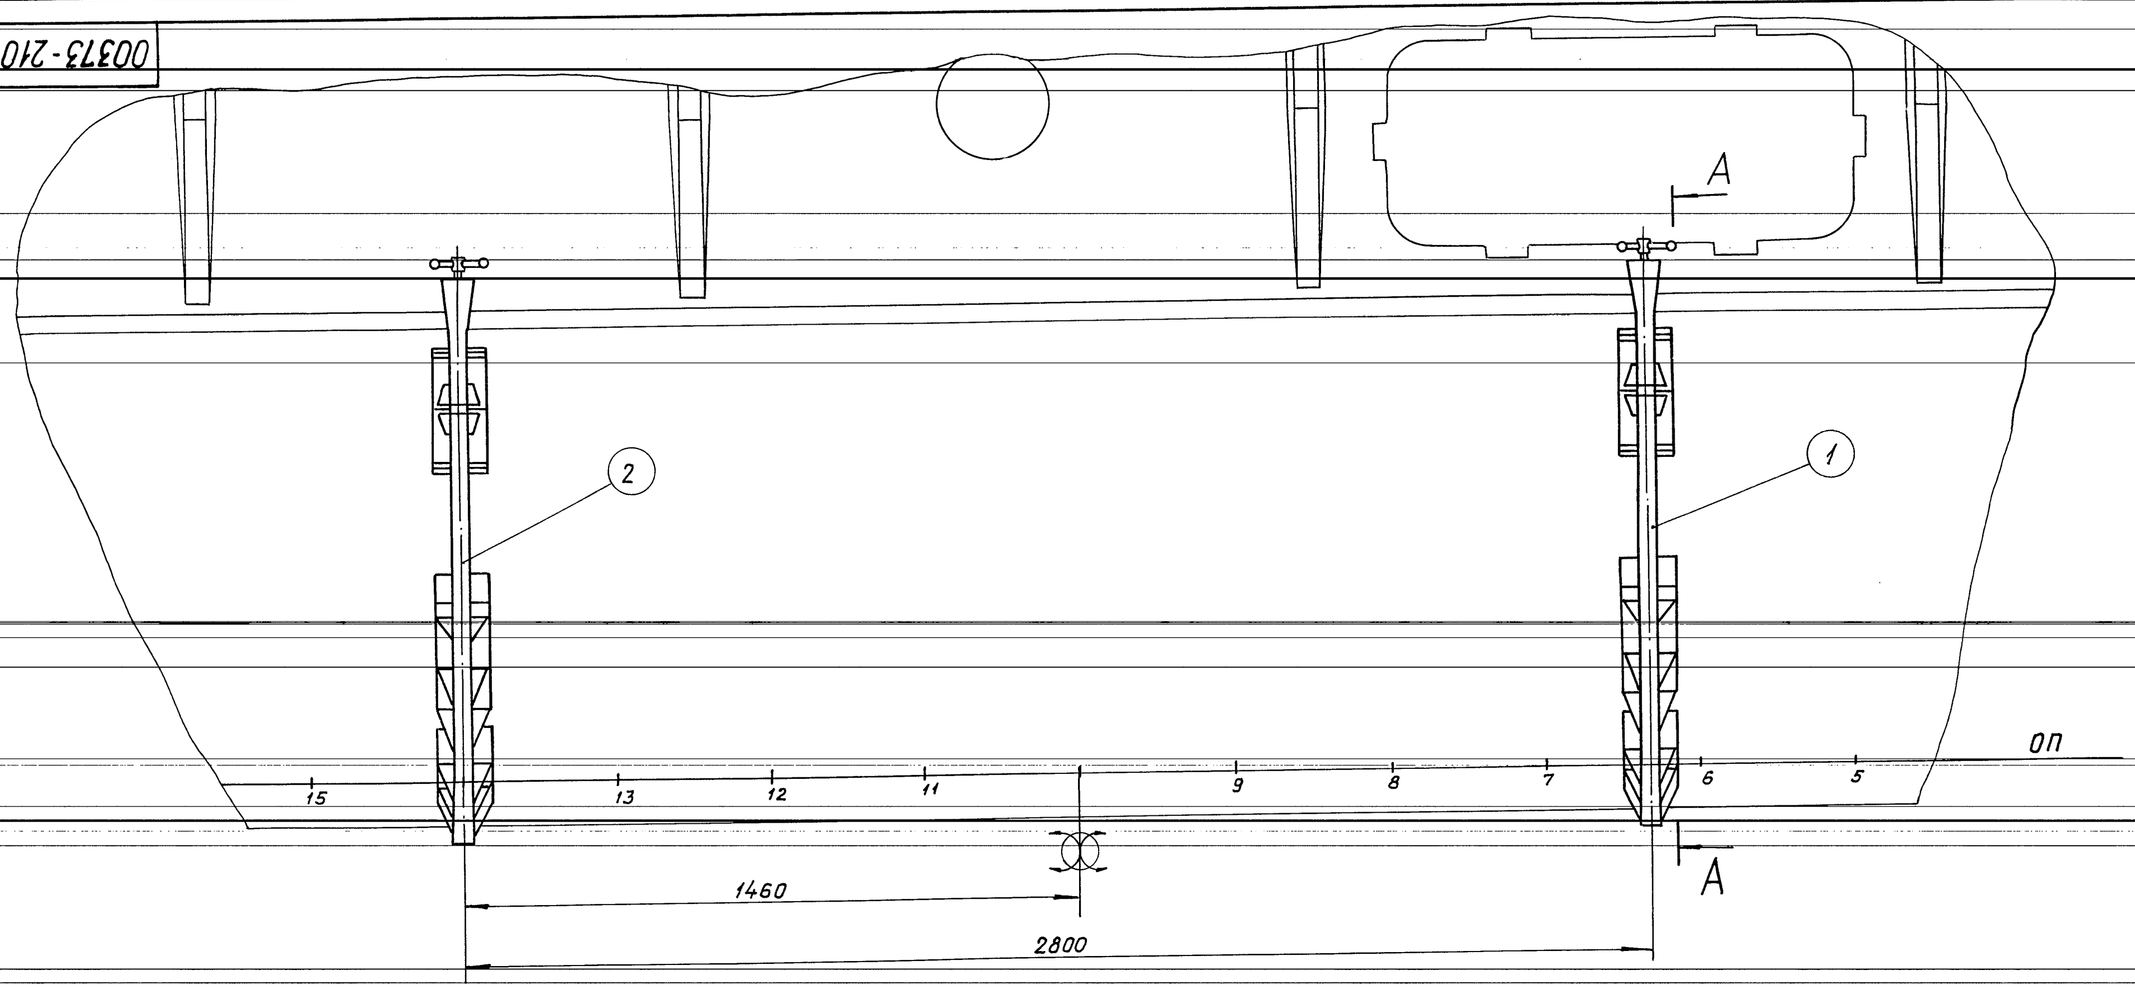

Вспомогательные документы	
Наименование	Обозначение
Теоретический чертеж наружного корпуса	00373-901-002
Конструктивный чертеж корпуса в сборе.	00373-101-002 СБ


1. Детали поз. 5 устанавливать по обеим бортам.
2. Предельные отклонения размеров $\pm \frac{IT14}{2}$.
3. Спусковые полозья проверить в действии установкой на шлюпку, закреплением и отдачей.
4. Покрытие крепежа по ОСТ 5. 9048-85.
5. В местах установки поз. 5 болты крепления наружного корпуса к жесткому закрытию не устанавливать.
6. * Отверстия под крепеж сверлить по детали поз. 5.
7. Спусковые полозья устанавливать по одному борту правому или левому – по согласованию с заказчиком.
8. Стопорение поз. 7, 8 по РД. 5. 9307-79 вид 9 или 15.3.
9. Поз. 7 допускается применять болты М8×35 ГОСТ 7798-70

А-А

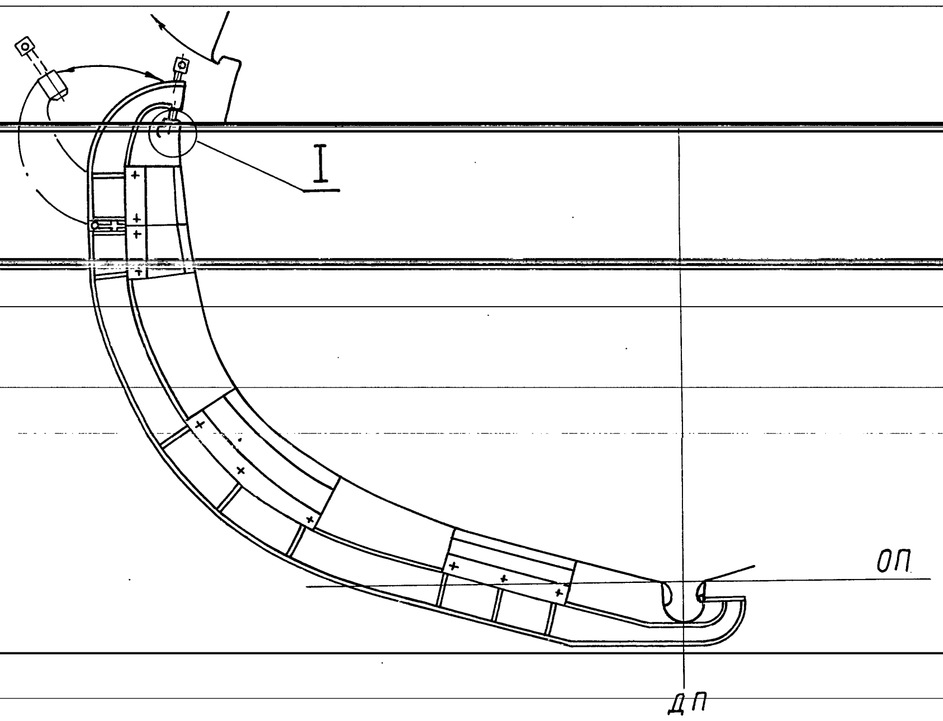

I

М1:2

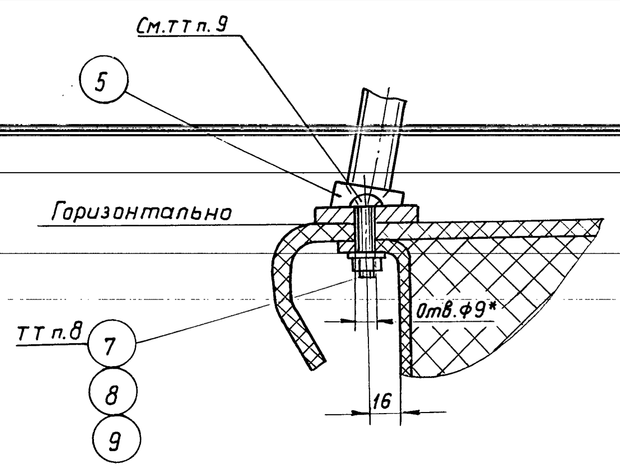

Одобрено:
Ст. инженер-инспектор Инспекции Регистра СССР Балтийского бассейна
Подпись 16.01.86. /Маркелов К.В./

Восстановлен с подлинника
Верно: Подпись Кузнецова Фамилия 9.01.93 Дата

Согласовано: 211 с Подпись /Ермолов/.
213 с Подпись /Гаврилов/.

Метролог: Подпись /Афанасьев/.

Инв. № подл.	Подпись и дата	Взам. инв. №	Инв. № дубл.	Подпись и дата
6781/9	Подп. 20.01.86.			

00376.365271.001 СБ

(00373-210-084 СБ)

Изм.	Лист	№ докум.	Подпись	Дата
Б		00373.21.368	Подп.	29.9.32.
Разраб.			Подп.	2.01.86.
Провер.		Лизунов	Подп.	9.01.86.
Т. контр.		Макиевский	Подп.	16.01.
Вып.		Недопь	Подп.	86.
Н. Контр.		Орлов	Подп.	17.1.86.
Утв.		Гурьянов	Подп.	16.1.86.

Установка спусковых полозьев

Лит.	Масса	Масшт.
	41,4	1:10
Лист	Листов 1	

Формат А1 пл. 0,5 м²